Portfolio

Filippo Antonio Visentin

About me



Sono Filippo Antonio Visentin, designer del prodotto e d'interni, attualmente studente al Politecnico di Milano.
La mia ricerca progettuale muove dall'osservazione delle interazioni tra le persone e dei modi reali in cui spazi e oggetti vengono abitati e utilizzati, che assumo come punto di partenza affinché la forma derivi dall'uso e non lo preceda.

Interpreto il design come un gesto che accompagna l'esperienza anziché imporsi, e ricerco l'equilibrio tra rigore tecnico e qualità materica.
Materiali e luce sono per me strumenti progettuali, che impiego per conferire calore e carattere, mentre il riferimento alla natura si traduce in un linguaggio contemporaneo.

Con la magistrale in Interior Spatial Design vorrei approfondire e specializzarmi sulle tecniche e le modalità progettuali che regolano questo settore e le sue varie declinazioni, poichè esse influiscono molto e possono cambiare il modo di vivere la quotidianità e non delle persone


Index

2° Anno



OltreEtrusco — Interior

3° Anno

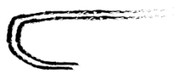


Bivacuum — Interior

2° Anno



Soundplace — Product Design

3° Anno

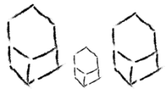


POLIEDRO — Interior / Product

2° Anno



Compluvio — Interior / Architecture

2024 - attuale

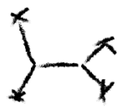

FPV — Product Design

OltreEtrusco

**Filippo Antonio Visentin, Anton Qerkini, Noè Bartolini,
Jacopo Dellanoce, Luca Mastromatteo**

Sconfinare è la metafora utilizzata per la progettazione dell'allestimento.

L'obiettivo è quello di far comprendere come la civiltà etrusca abbia sconfinata nell'era moderna grazie agli innumerevoli spunti di riflessione da essa derivanti.



Sono presenti artefatti **antichi** e **moderni**, messi a confronto in modo che sembrino gradualmente della stessa epoca. L'atteggiamento progettuale è stato intrapreso al fine di far coincidere la metafora spaziale e il tema di progetto.


Il confine visto come Oltre



Prima sala
Confine netto e definito, percorso obbligato

Seconda sala
Confine rotto a metà, percorso semi-libero

Terza sala
Confini distribuiti in tutto lo spazio, percorso libero

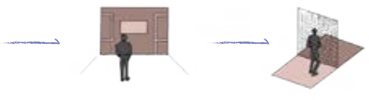

Quarta sala
Confine oltrepassato dal soggetto del quadro che torna ambiente


Quinta e sesta sala
Confine da oltrepassare attraverso i tendaggi sottili

Planimetria

Prima sala

Quotidianità I



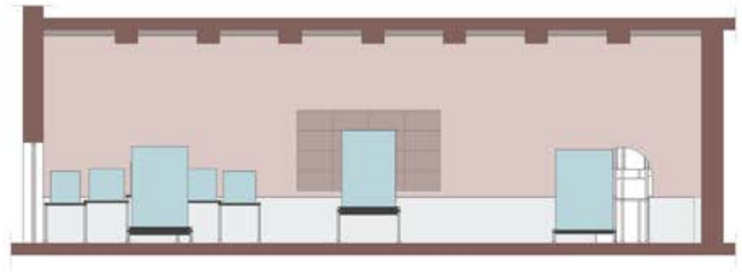

Sezione A-A' Scala 1:50

Planimetria


Seconda sala

Quotidianità II



Sezione B-B' Scala 1:50

Sezione C-C' Scala 1:50

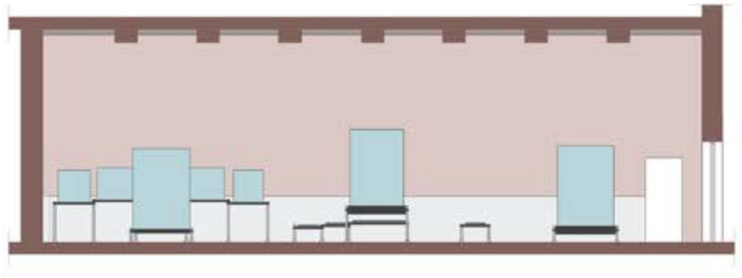


Sezione D-D' Scala 1:50

Planimetria

Terza sala

Arte e guerra

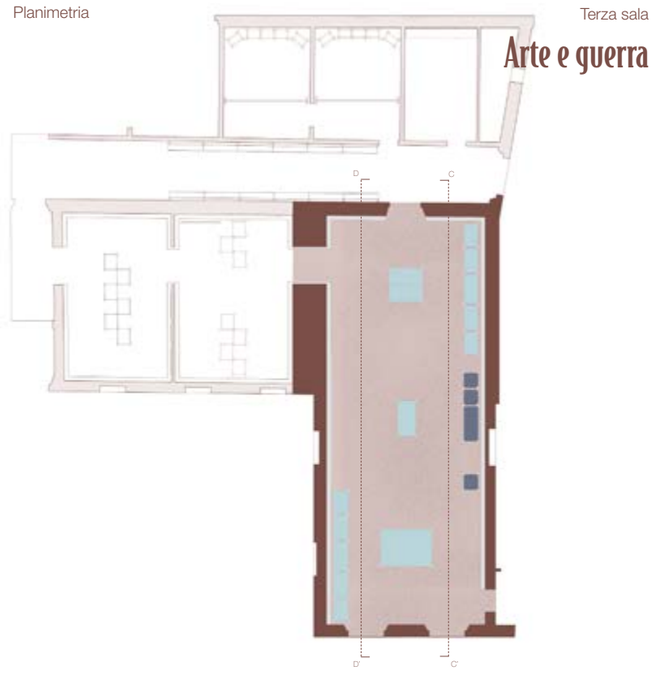


Quarta sala

La morte



Sezione E-E’ Scala 1:50

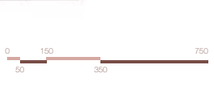

Quarta stanza






Struttura Oltre


Modularità
La base di partenza della struttura è composta da pochi elementi facilmente ripetibili e personalizzabili per adattarli a tutte le esigenze.


Facilità di installazione
La struttura risulta di facile installazione grazie alla presenza alle estremità di elementi regolabili in altezza per permettere un’aderenzaperfetta nelle zone a contatto con le superfici.

Costo contenuto
I componenti sono di materiale metallico quale acciaio Inox e alluminio in minima parte, il che rende il costo complessivo contenutorispetto ad altre soluzioni possibili.

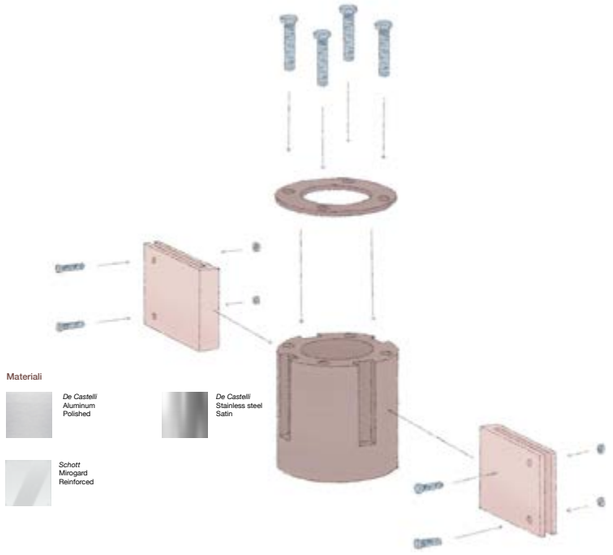


Totale componenti Oltre

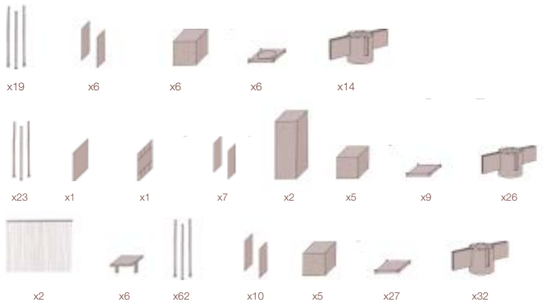


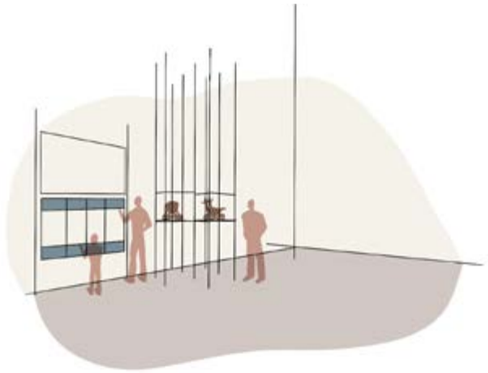

Scratch and sniff
Il pannello sensoriale interattivo permette di immergersi alla
scoperta delle fragranze dell’Era etrusca con un’aggiunta di modernità grazie alle rivisitazioni di quest’ultime. Lo spettatore
interagisce grattando la superficie in determinate aree per rilasciare il profumo selezionato.

Piattaforma girevole
Permettete al visitatore di ruotare lentamente certi artefatti per
scoprire e osservare anche le facce che normalmente sarebbero
nascoste alla vista.

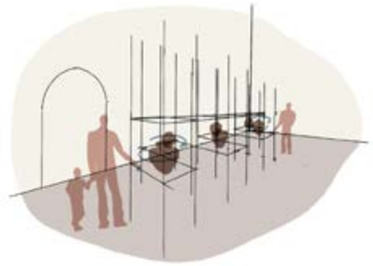

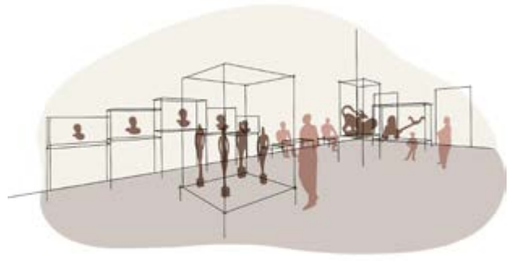




Sala 2

Sala 3



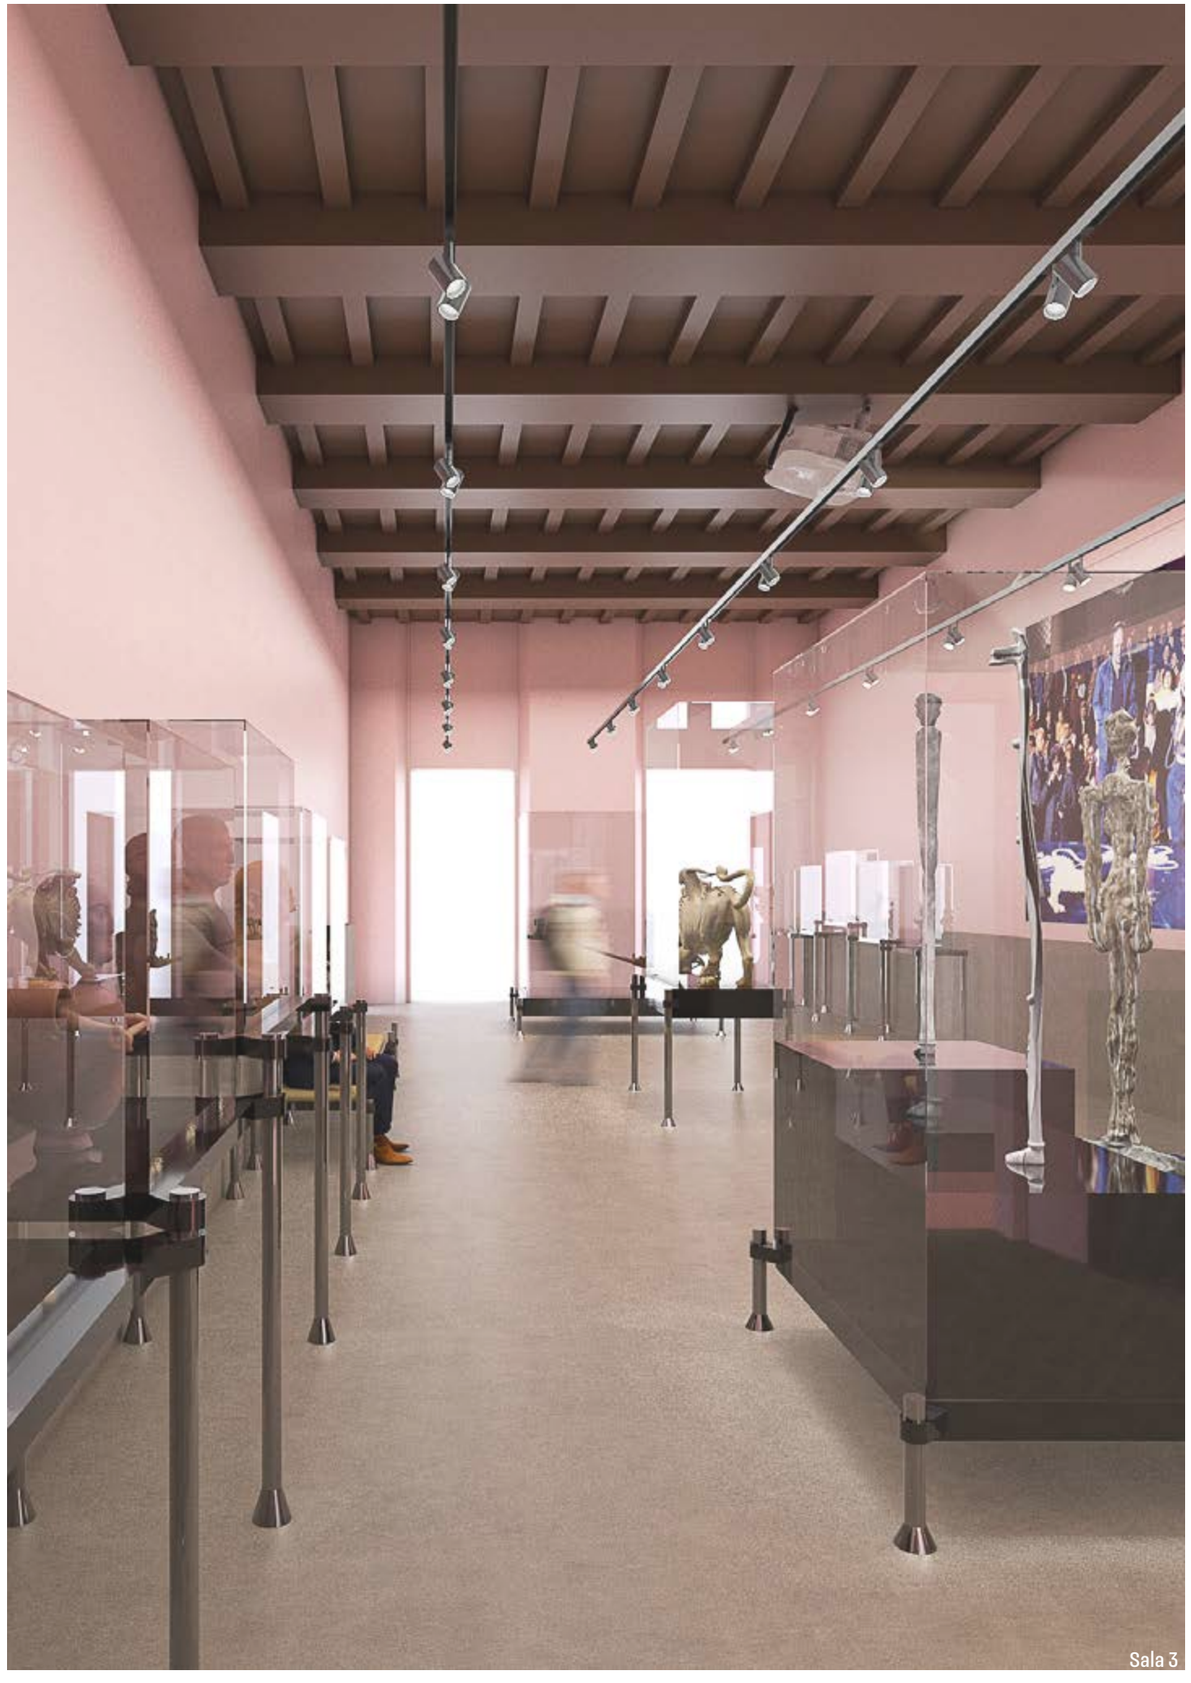

Sala 3

Bivacuum

Visentin Filippo Antonio, Anton Qerkini


Un bivacco **per tutti**.
Uno spazio che sia un rifugio per tutti, per almeno 8 persone.
Un bivacco standard, **preassemblato**, di facile trasporto e con il minimo montaggio in loco.

Un rifugio pensato ad un'altitudine massima di 2000 m s.l.m. e locata su terrazzi naturali o zone a ridotta pendenza, un bivacco **all-season** adattabile a tutti i periodi dell'anno.

Uno spazio intuitivo da usare e dove **auto-organizzare** lo spazio liberamente. Un rifugio situato su uno spiano naturale panoramico, sul sentiero per la cima della Grignetta, ad un'altitudine raggiungibile a livelli **escursionistici**.




Una **griglia modulare** a soffitto permette di disporsi liberamente nello spazio, e di attaccare amache per dormire, sfruttando lo **spazio verticale**.
Tavoli **a scomparsa** sulle paretiche nascondono sedute pieghevoli.

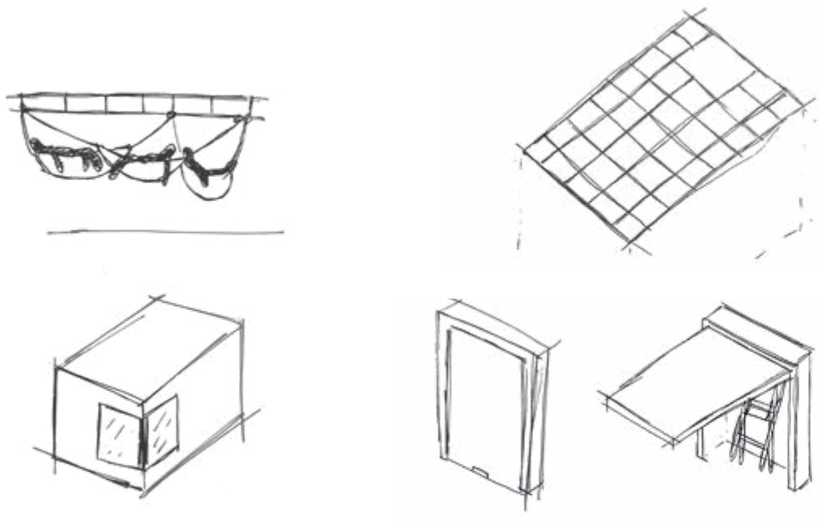




Fronte bivacco

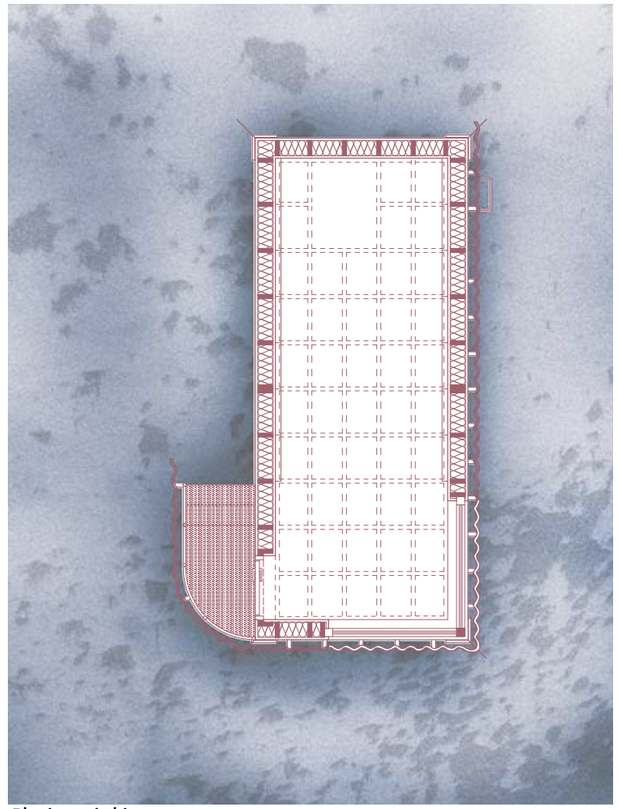

Planimetria bivacco

Sezione lato bivacco

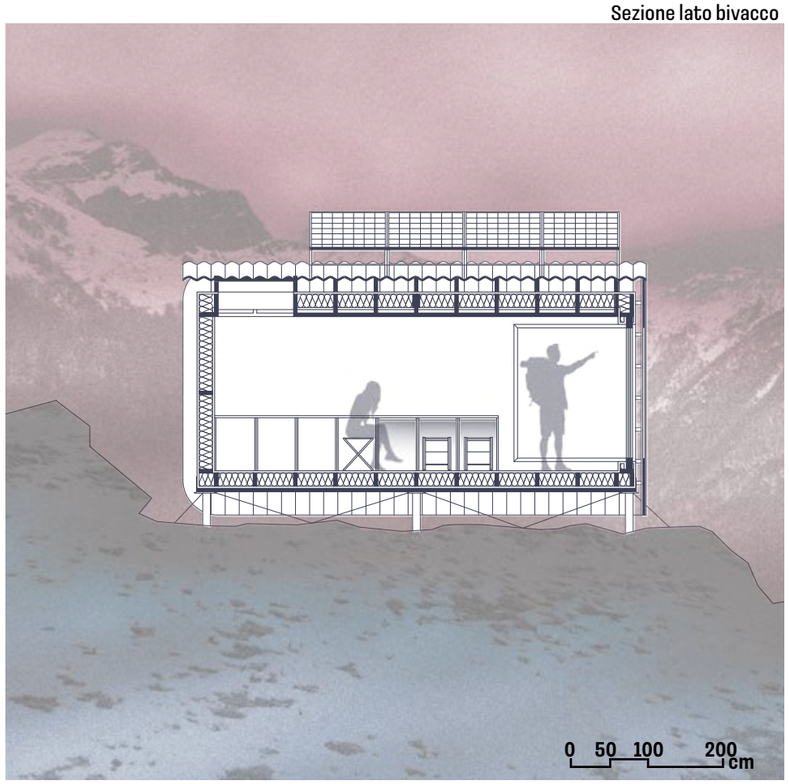


Sezione lato bivacco



Relazione tecnica

Pannelli fotovoltaici a inclinazione regolabile:

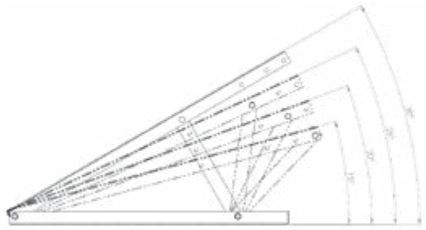

• Quattro pannelli 110 x 180 cm, montati sul tetto su supporti fino a 30° di inclinazione

Stratificazione dell'involucro dall'interno:

• Pannelli in legno compensato 1.5 cm


• Struttura **baloon frame** in legno, passo 57.3 cm

• Vuoto tecnico 3 cm


• Barriera al vapore e isolamento in lana di pecora 16cm

• Camera ventilata 3 cm

• Pannelli in metallo 0.5 cm

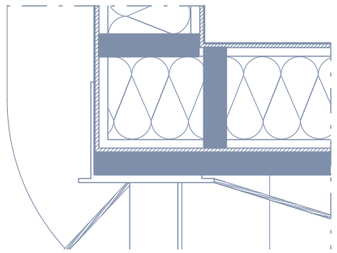

Telaio, fondazioni a vite e cavi

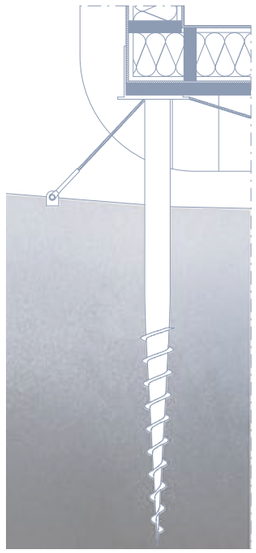

• Telaio di base strutturale in metallo, passo travi 42.8 cm

• Viti in acciaio di diametro 11 cm e lunghezza 193 cm

• Cavi di diametro 1 cm a 45°



Dettaglio telaio e finestra

Binario in alluminio:

• Binario che permette il fissaggio di un gancio estraibile e configurabile nella posizione in base alle necessit' dell-utente.

• Presenza di una bassa elettrificata che tramite contatto provvede alll'alimentazione delle luci se neces-sario.

• La posizione dei ganci e possibile in qualsiasi punto in cui sia presente un binario.






Esterno bivacco

Interno bivacco



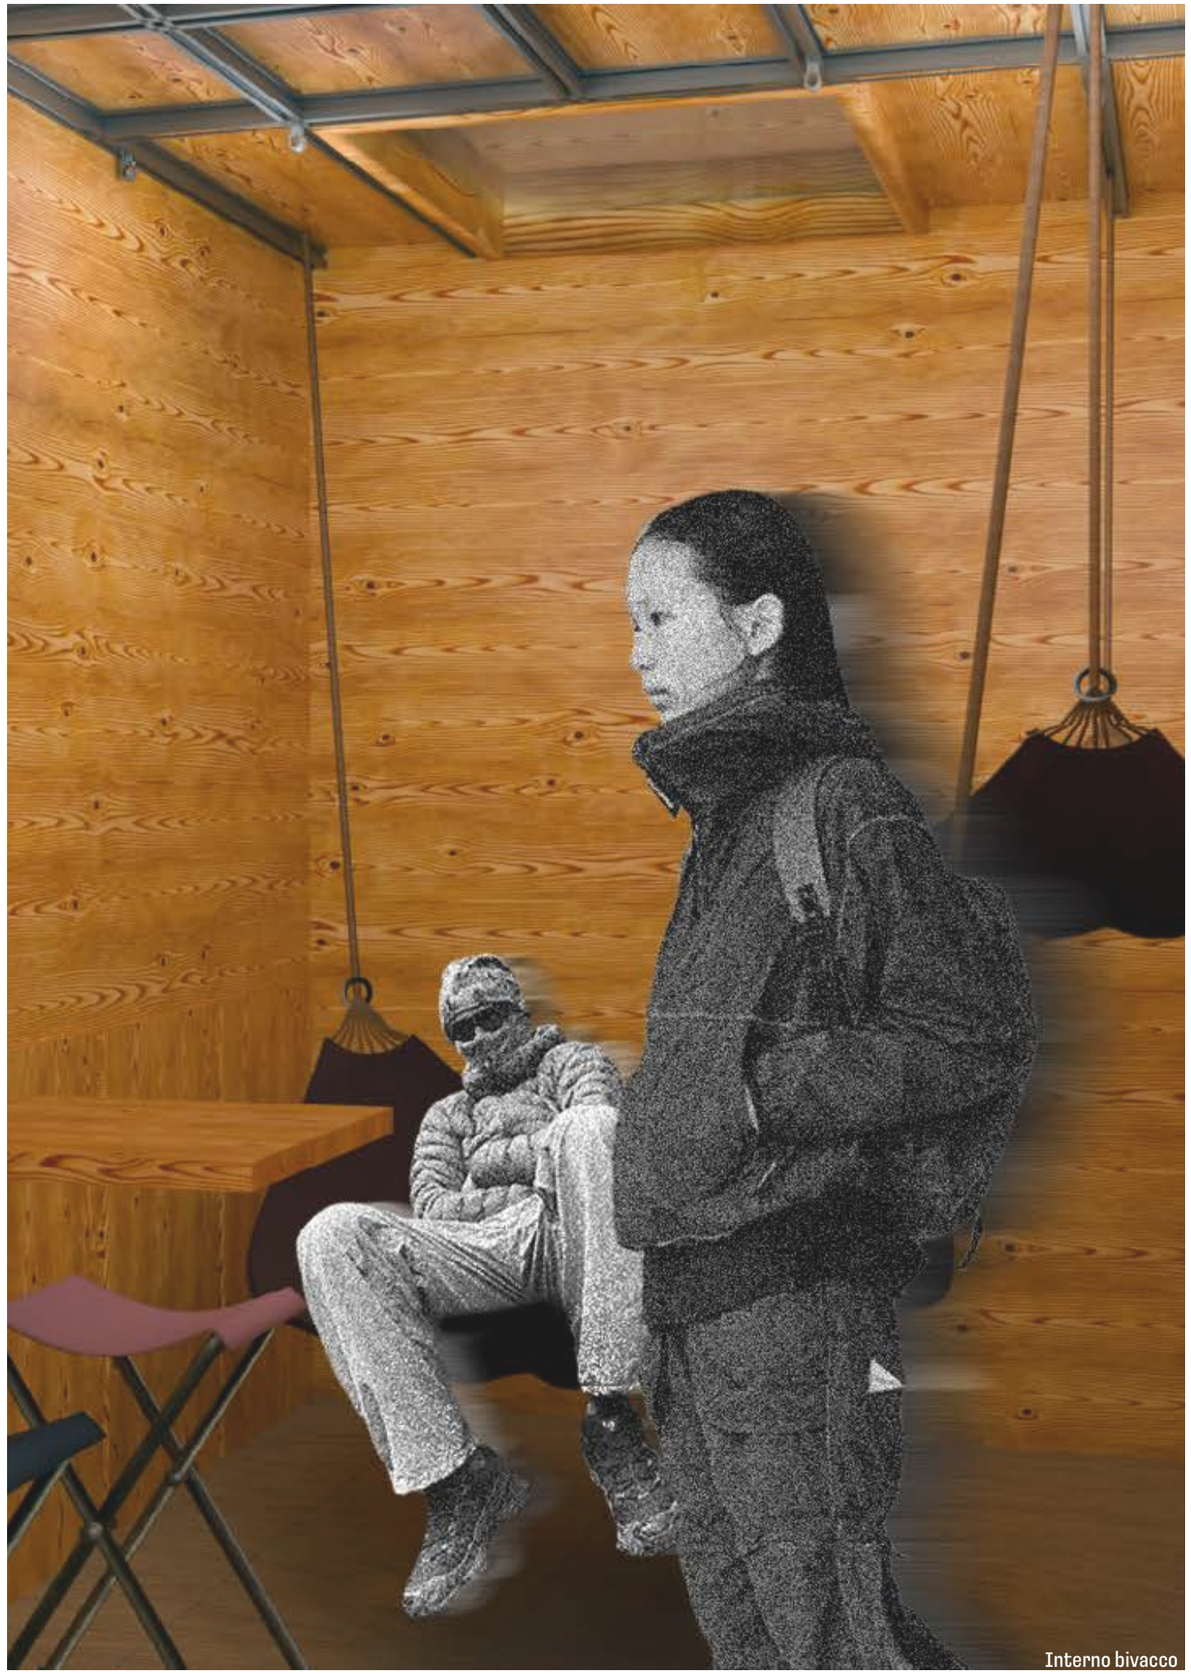

Interno bivacco

Soundplace

Visentin Filippo Antonio, Francisco Junior Cuello Ramirez, Monow Sarkar

Soundplace e un arredo urbano interattivo nato per favorire l'**incontro** e la **condivisione** attraverso la musica.
Ispirato ai risultati di un'indagine sul territorio di Morbegno, risponde alla mancanza di spazi autogestiti per l'aggregazione giovanile.

Crazie alla sua funzione di cassa di **risonanza analogica**, amplifica il suono di uno smartphone senza energia elettrica.

Il progetto trasforma un semplice oggetto in un punto di ritrovo
accessibile e partecipativo, un luogo dove la musica diventa occasione di incontro, proprio come un falò attorno al quale le persone si riuniscono



Marco ha visto che manca posco al suo compleanno e vuole organizzare una **festa**



Un suo amico gli ha suggerito il servizio Suondplace. Prenota il servizio attraverso l'**app**.



Arrivando alla location vedono l'inserto e attraverso le **grafiche** illustrate capiscono come utilizzare il servizio .



L'esperienza ha inizio e tutti i partecipanti si godono la **musica** trascorrendo una piacevole serata.




Il giorno dopo Marco ripensa ai bei momenti vissuti e decide di lasciare un' ottima **recensione**.



Luogo


Ponte Vanoni, Morbegno , Italia



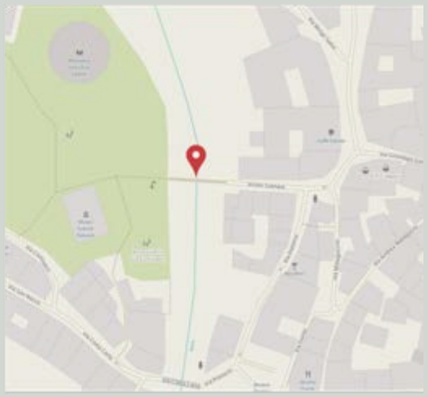

Il progetto nasce da un sondaggio condotto a **Morbegno**, dal quale è emersa la carenza di spazi autogestiti dedicati all'**aggregazione giovanile** e alla **pratica musicale**.

Per rispondere a questa esigenza, abbiamo ideato un Walking Tree di 80 × 160 cm, pensato come elemento di arredo urbano **interattivo**.

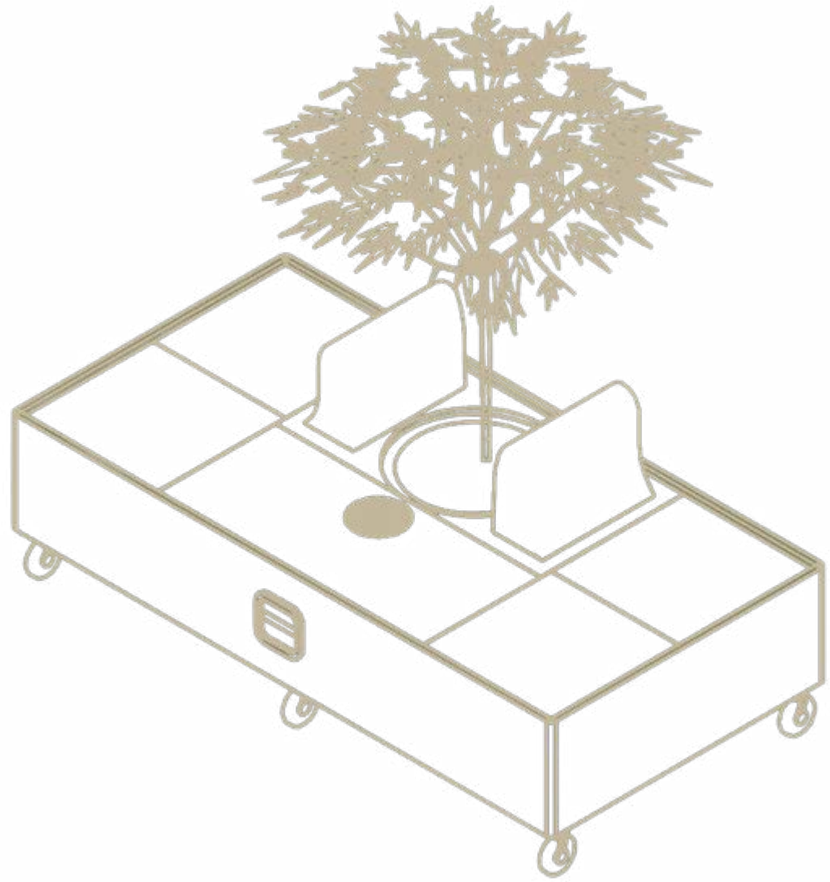


Soundplace funziona come una cassa di **risonanza analogica**: inserendo uno smartphone nell'apposita bocchetta, il suono viene amplificato senza l'utilizzo di energia elettrica.

Il nome unisce "sound" e "fireplace", evocando l'idea di persone che si ritrovano attorno alla **musica** come intorno a un falò.


Scheda montaggio

Componenti


Disegni in scala 1:50

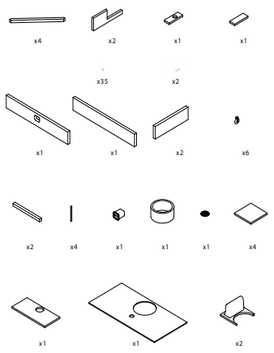


Disegni in scala 1:25

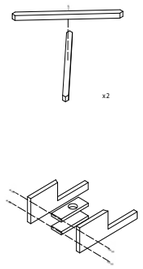


Disegni in scala 1:25

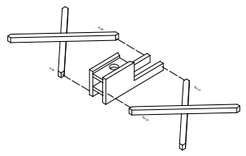


Disegni in scala 1:25

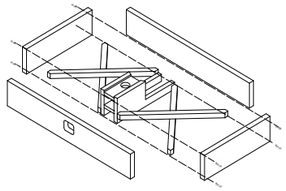


Disegni in scala 1:25

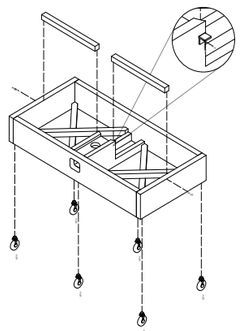


Disegni in scala 1:25

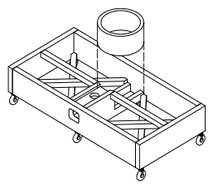


Disegni in scala 1:25

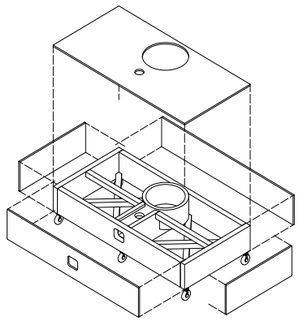


Disegni in scala 1:25

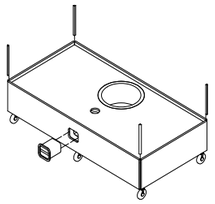


Disegni in scala 1:25

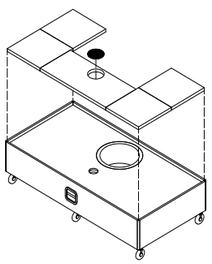


Disegni in scala 1:25

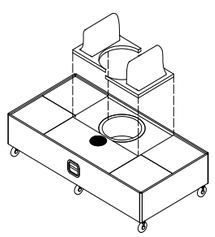

Disegni in scala 1:25

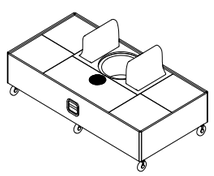

Disegni in scala 1:25

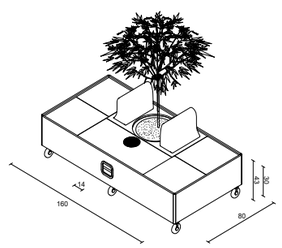



Compluvio


Visentin Filippo Antonio

La copertura è il dispositivo.


Due volte vetrate dal profilo morbido incontrandosi al centro dell'edificio e piegandosi verso l'interno, come il tetto di una domus romana: è la forma stessa a intercettare la pioggia e a condurla, per sola **gravità**, verso il compluvio centrale.


All'interno il ciclo continua, una rete di irrigazione a bassa pressione riporta l'acqua della ùcisterna alle vasche di coltura; le piante la restituiscono all'aria traspirando, il vapore **condensa** sul vetro e scivola lungo la curvatura fino a rientrare nel circuito. Nessuna goccia lascia il sistema: la serra non consuma acqua, la **trattiene** e la **fa girare**.


Il fabbisogno esterno si riduce così al solo reintegro delle perdite, e un edificio di produzione diventa un **sistema** quasi **chiuso**, in cui forma architettonica e ciclo dell'acqua coincidono.

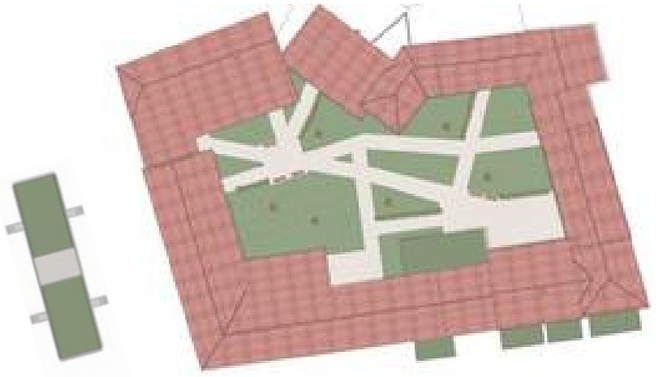

Il luogo: Cascina Linterno, Milano

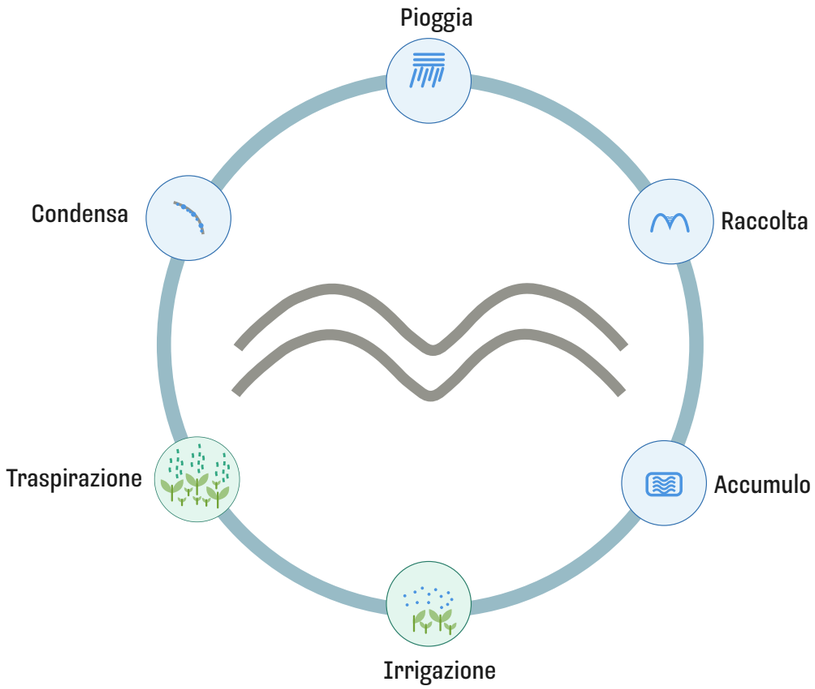

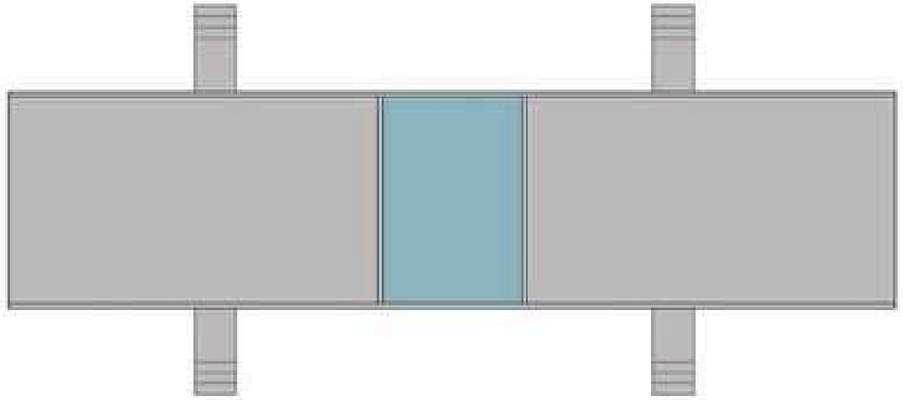

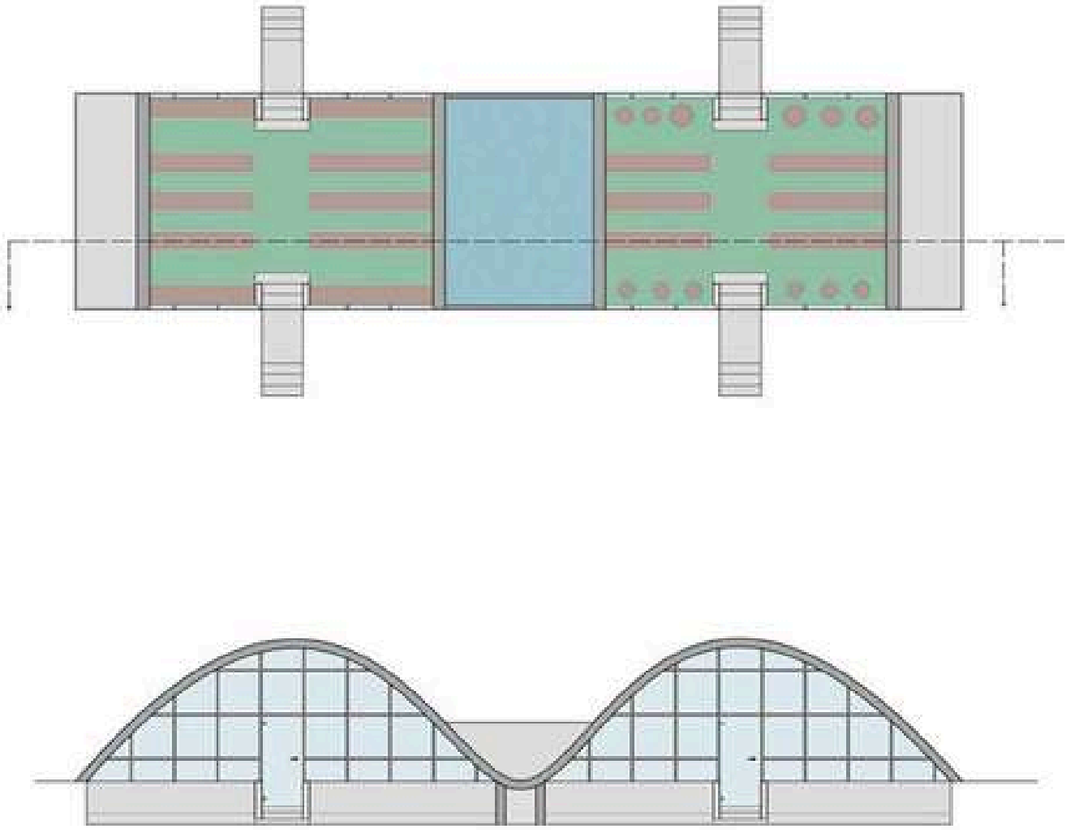



Esterno bivacco

Interno bivacco





Interno bivacco

POLIEDRO

Filippo Antonio Visentin, Lawrence Sedra, Anna Varsavia, Nina Rosa Patanè

Lo spazio non impone: guida.
Al centro ci sono le persone: da questi primi segni il concept inizia a prendere forma, lasciando che gli incontri emergano in modo naturale.


POLIEDRO è un progetto dedicato a favorire l'interazione sociale tra i giovani.

Concepito come sistema di **sedute modulari**, si compone di una panca e di un elemento doppio che, assemblati in configurazioni flessibili, danno vita a piccole "isole sociali".

A completarle è una **lampada integrata**: una sorgente di luce discreta che accentua intimità e calore, estendendo la sensazione di presenza condivisa anche nelle ore serali.

Ispirato alla geometria organica delle **rocce basaltiche** irlandesi, il progetto traduce l'aggregazione naturale in un linguaggio urbano contemporaneo, invitando le persone a riunirsi, sostare e connettersi.



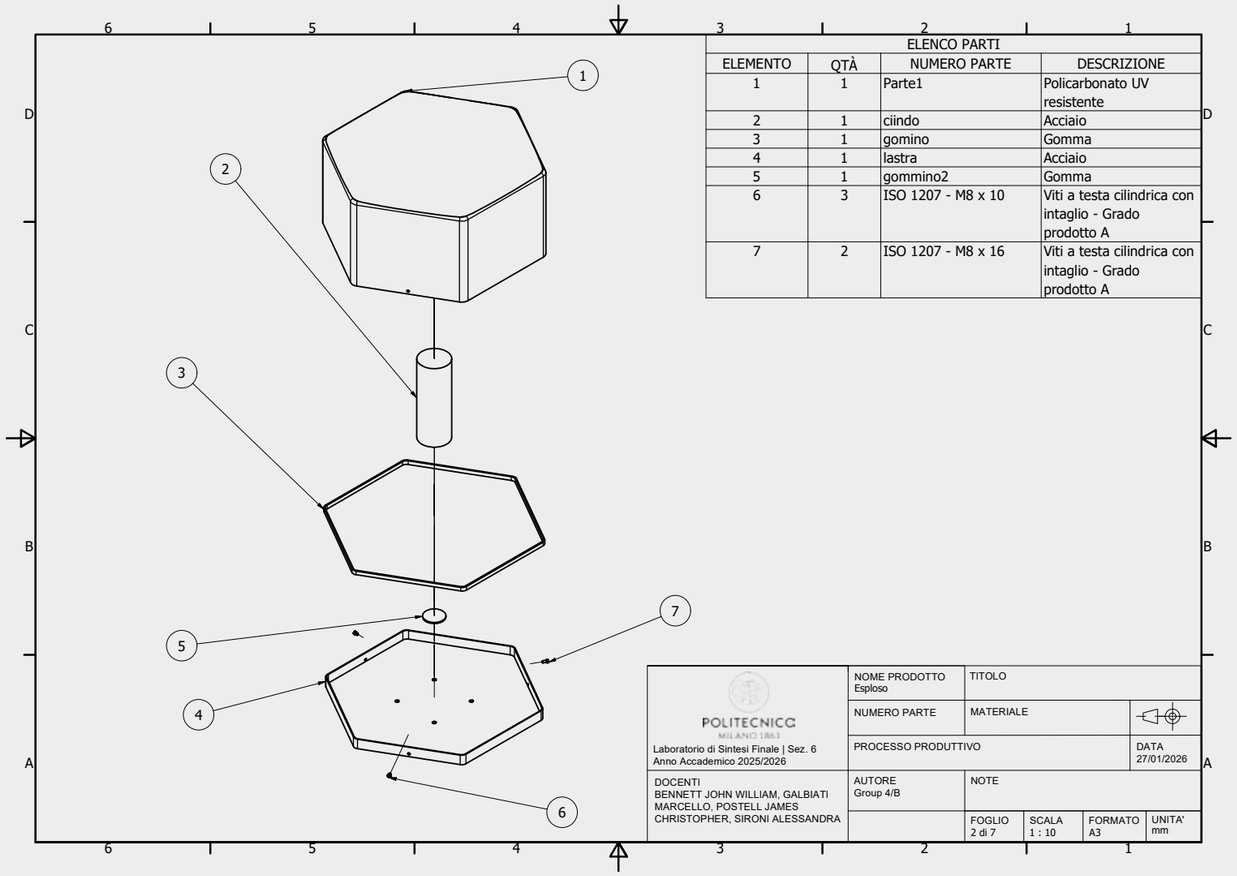

ELENCO PARTI			
ELEMENTO	QTÀ	NUMERO PARTE	DESCRIZIONE
1	1	Parte1	Policarbonato UV resistente
2	1	ciindo	Acciaio
3	1	gomino	Gomma
4	1	lastra	Acciaio
5	1	gommino2	Gomma
6	3	ISO 1207 - M8 x 10	Viti a testa cilindrica con intaglio - Grado prodotto A
7	2	ISO 1207 - M8 x 16	Viti a testa cilindrica con intaglio - Grado prodotto A

POLITECNICO MILANO 1863
Laboratorio di Sintesi Finale | Sez. 6
Anno Accademico 2025/2026

NOME PRODOTTO: Esploso	TITOLO		
NUMERO PARTE	MATERIALE		
PROCESSO PRODUTTIVO		DATA: 27/01/2026	
DOCENTI: BENNETT JOHN WILLIAM, GALBIATI MARCELLO, POSTELL JAMES CHRISTOPHER, SIRONI ALESSANDRA	AUTORE: Group 4/B	NOTE	
	FOGLIO: 2 di 7	SCALA: 1 : 10	FORMATO: A3 — UNITA': mm


POLIEDRO lamp

La lampada POLIEDRO, dalla forma esagonale, è progettata per svolgere anche la funzione di piccolo tavolo ed è pensata per essere collocata al centro della composizione della panca.

La sua **doppia funzione** rafforza l'idea dell'uso condiviso: agisce insieme come superficie d'appoggio e come punto focale dell'interazione sociale. Il guscio esterno è realizzato in policarbonato, abbinato a una base in cemento e a una piastra in alluminio che ospita i componenti elettronici.

La lampada rappresenta al tempo stesso la sorgente luminosa fisica e il calore simbolico che anima il progetto, diventando un elemento **centrale** che valorizza socialità, aggregazione ed esperienza condivisa.



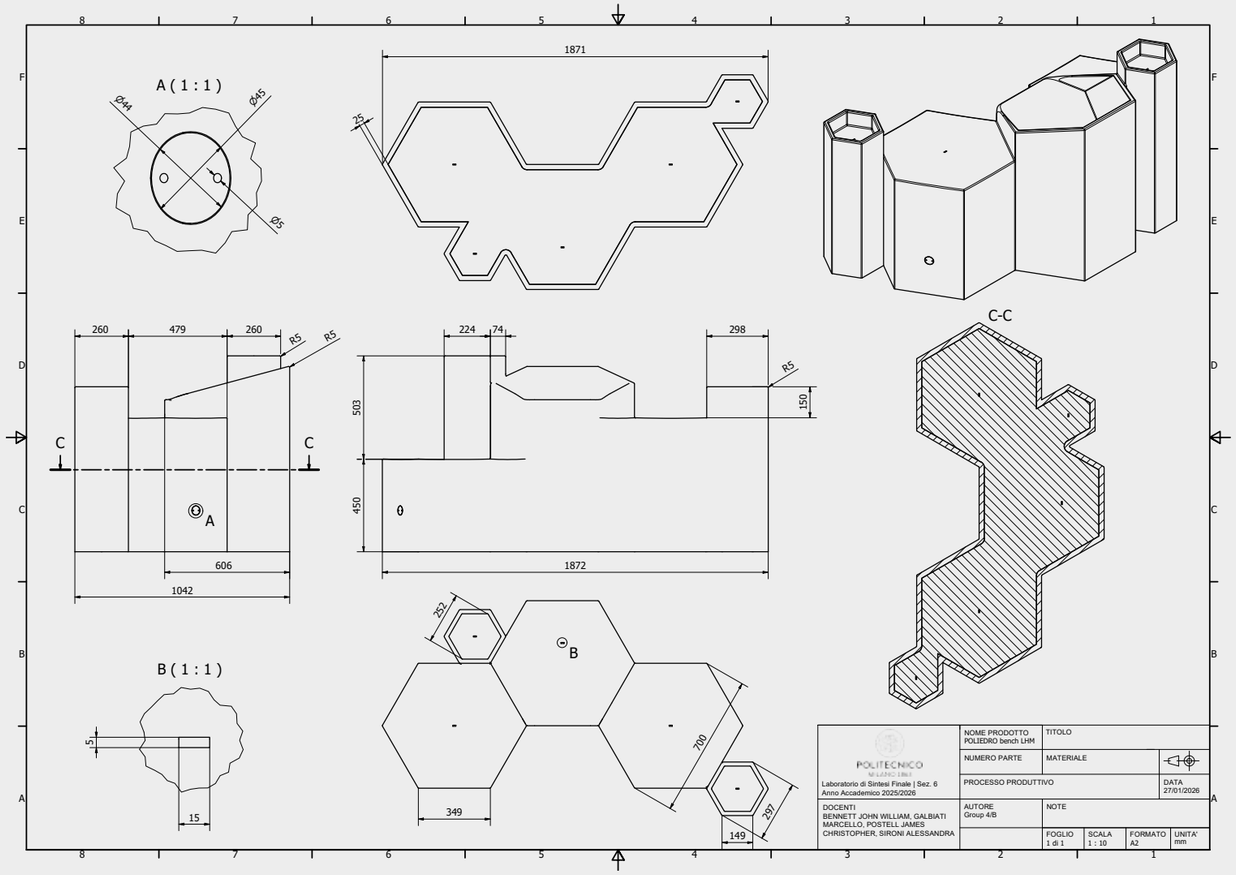


Composizione sedute



POLIEDRO bench

Concepita secondo la stessa logica progettuale, la panca POLIEDRO è una seduta di grandi dimensioni composta da sei unità modulari, disposte con cura per favorire l'interazione sociale e l'uso condiviso.

La configurazione è pensata per incoraggiare l'aggregazione, trasformando il sistema di sedute in un'esperienza collettiva più che in un oggetto puramente funzionale. Due delle unità presentano un profilo di seduta dedicato, studiato appositamente per migliorare l'ergonomia e massimizzare comfort ed efficienza.

La panca integra le stesse soluzioni tecniche delle singole unità: i fori di drenaggio, progettati per garantire un efficiente deflusso dell'acqua, e una scanalatura circolare sulla superficie superiore, che facilita la movimentazione e il trasporto, incorporando in modo naturale i requisiti funzionali nel disegno complessivo.




Dettaglio seduta


A matter of presence


La mostra immersiva “A matter of presence” vuole creare nel visitatore una sensazione di trovarsi all’interno di una montagna all’origine della terra, nei meandri di un vulcano.

L’obiettivo principale è l’esposizione della serie di sedute
modulari POLIEDRO attraverso la creazione di uno spazio poco illuminato e circondato da specchi per amplificare il concentto di modularità e di composizione di pattern che le sedute hanno come obiettivo quello di crearlo.

Al centro della stanza è presente una zona che vuole creare l’ideale composizione del prodotto , vuole inoltre anche essere il punto nevralgico e di interazione.

Crazie all’utilizzo di tende che coprono lo spazio e le aperture verso l’esterno vi è la possibilità di ricreare un’atmosfera poco illluminata, molto immersiva e che vuole richiamare il crepuscolo e quel-la sensazione di caldo interiore che ognuno sente quando si avvicina ad una sorgente calda.

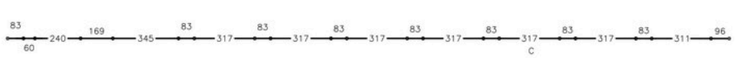

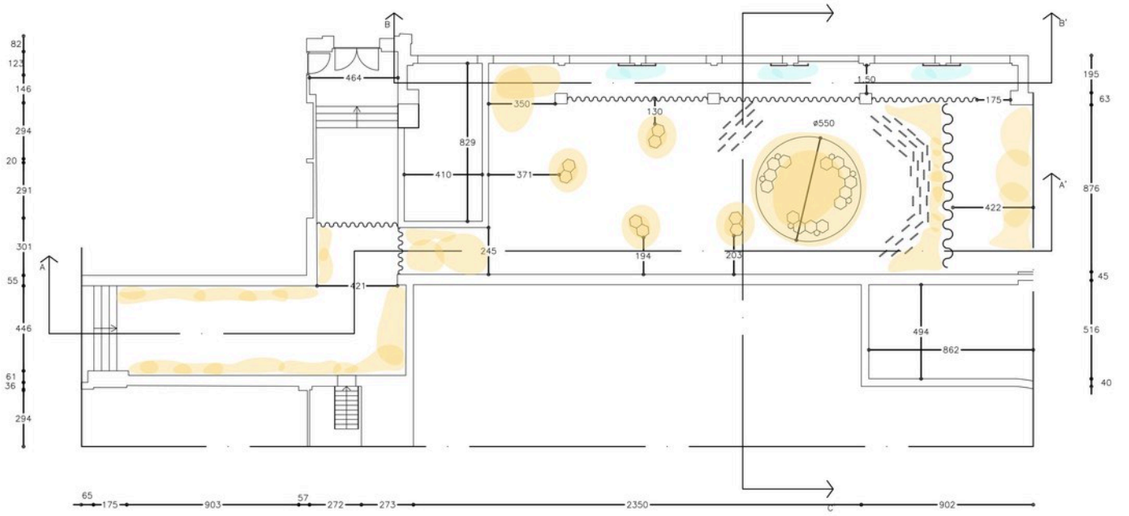

Planimetria illuminazione

Varo 80s




LED
3000 K
CRI ≥ 90
L80 / 50000 h
≤ 2 SDCM (initial MacAdam)

LINEA opal



LED
3000 K
CRI ≥ 97 -90
L95 / 50000 h -L85 / 50000 h
≤ 3 SDCM (initial MacAdam)
R : 102 -99 | R : 96 -91 | R : 96 -

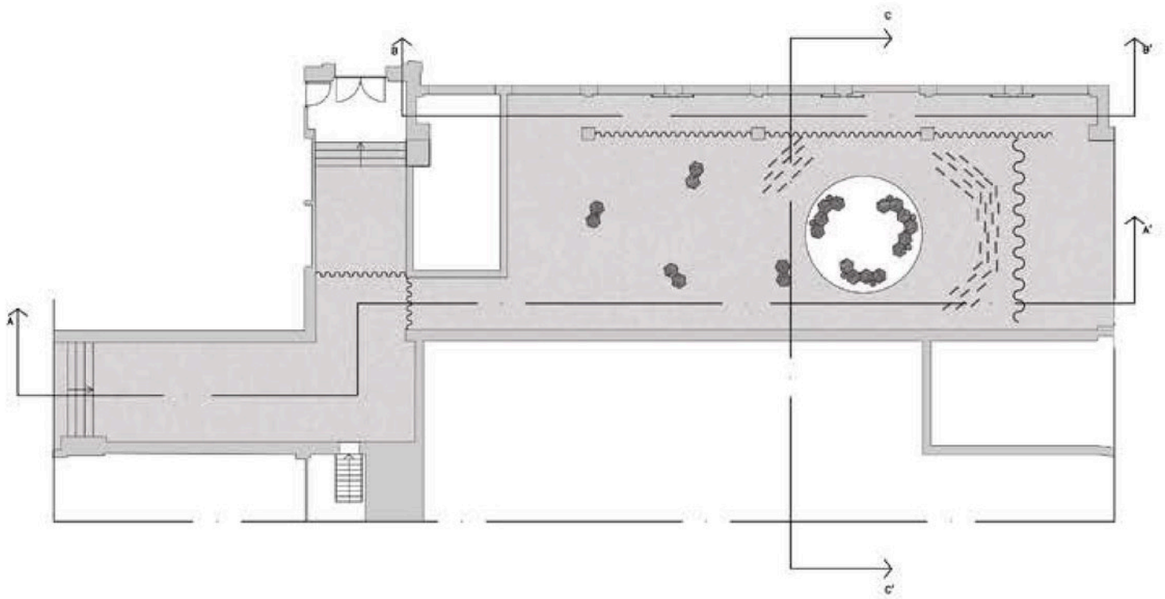

Sezioni sala espostitiva



Planimetri sala espositiva



Interno sala



Interno sala



Interno sala

FPV (First person view)


Visentin Filippo Antonio, Mattia Soffiato

Il progetto nasce da un problema strutturale puro: costruire un oggetto volante capace di sopportare ***urti*** *ripetuti mantenendo un* ***peso minimo****.*
Un drone FPV è una macchina nervosa, sottoposta a sollecitazioni violente e discontinue; il suo telaio è il punto in cui prestazione e integrità si contendono ogni millimetro di materia. Rigidezza torsionale, assorbimento degli impatti, protezione delle eliche: tutto dentro un budget di pochi grammi.

Il processo è stato interamente iterativo. La geometria, modellata parametricamente, è passata attraverso cicli successivi di stampa FDM, test in volo e revisione: i primi prototipi hanno rivelato punti di rottura nei bracci in corrispondenza dei motori, risolti ispessendo le sezioni critiche e orientando la stampa lungo le linee di sforzo principali.
Le paraeliche, inizialmente pensate come anelli pieni, sono evolute in strutture alleggerite a nervature: la materia rimane solo dove la fisica la richiede.

Parallelamente allo sviluppo strutturale, il progetto ha affrontato il cuore elettronico della macchina: la scheda dei circuiti è stata disegnata ***su misura*** *per il telaio, definendo layout dei componenti, tracciati e punti di fissaggio in dialogo diretto con la geometria stampata. Forma e funzione sono cresciute insieme: il telaio ha modellato la scheda, la scheda ha vincolato il telaio. Per la produzione ci si è affidati a un'****azienda esterna*** *specializzata una scelta che ha introdotto nel processo la logica reale della filiera: preparare file esecutivi corretti, rispettare tolleranze e standard industriali, verificare al ritorno la corrispondenza tra disegno e prodotto.*
La scelta del materiale ha seguito la stessa logica del compromesso: sufficientemente rigido da mantenere la geometria in volo, sufficientemente duttile da deformarsi nell'impatto invece di frantumarsi. Ogni crash è diventato dato di progetto: ***la rottura non come fallimento ma come informazione****, il prototipo come strumento di misura.*

*Il risultato è un oggetto che tiene insieme due modi di produrre: l'****autoproduzione*** *della stampa 3D riparabile, ristampabile in poche ore e la precisione industriale della componentistica su commessa. Un ibrido che restituisce al pilota il controllo completo sulla propria macchina: progettarla, romperla, capirla, ristamparla.*

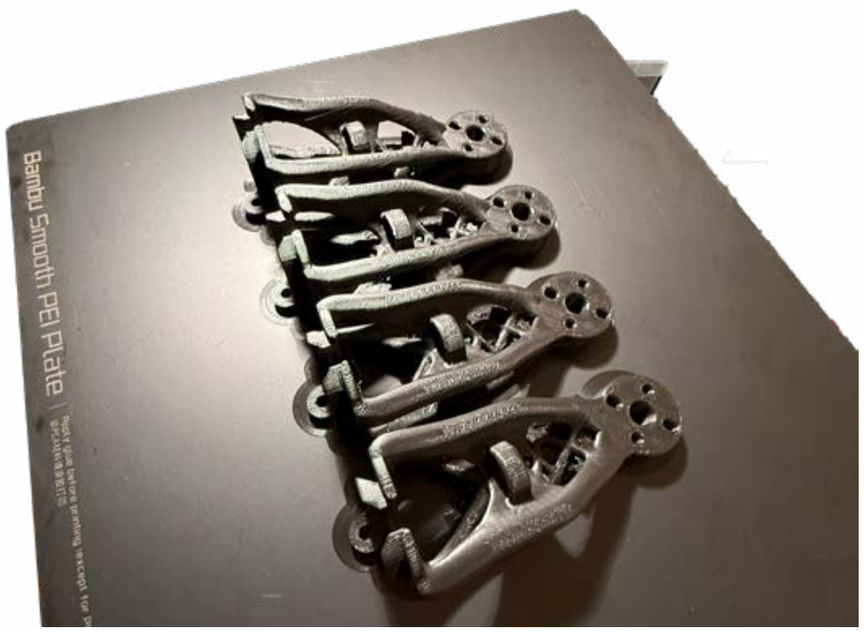

Prototipo protezione rotori




Fpv assemblato con protezioni in TPU


Para eliche


FPV Drone Frame medium size


FPV Drone Frame medium size


Leva chiusura lavatrice industriale LG

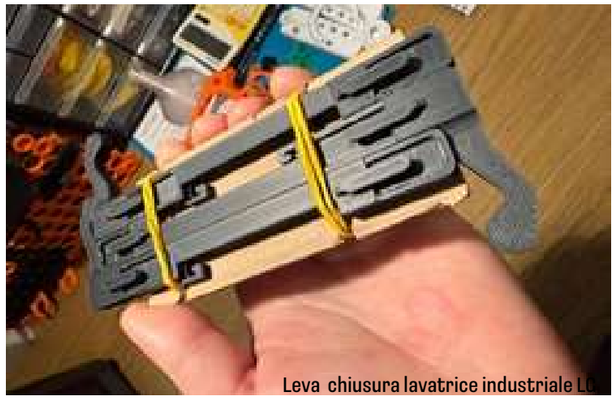
Leva chiusura lavatrice industriale LG


Elemento apertura sportello forno Samsung


Elemento apertura sportello forno Samsung


